by William

Based on plans provided showing ceiling at 9 ft.
Confirm finished height including wood/carpet floor
before final. Site measure after drywall and flooring required.

Wood border around recessed leather pad

Add 2" strapping to entrance door jamb width. 32 3/4" depth from rear closet.

Reframe to allow for built ins
Remove door frame at closet.

door installed
extension

Wiring chase
Low voltage

Switch location

Linnen closet

Washroom
208

Controls

Bedroom
207

Hewn wood jamb with shadow reveal

Drywall and Piant

H - 43
S - 55.75

Fabi Residence - Bedroom Plan


Scale: 3/4" : 1'


Sept 8,2026

Plan view - 207.0

by William

Based on plans provided showing ceiling at 9 ft.
Confirm finished height including wood/carpet floor
before final. Site measure after drywall and flooring required.

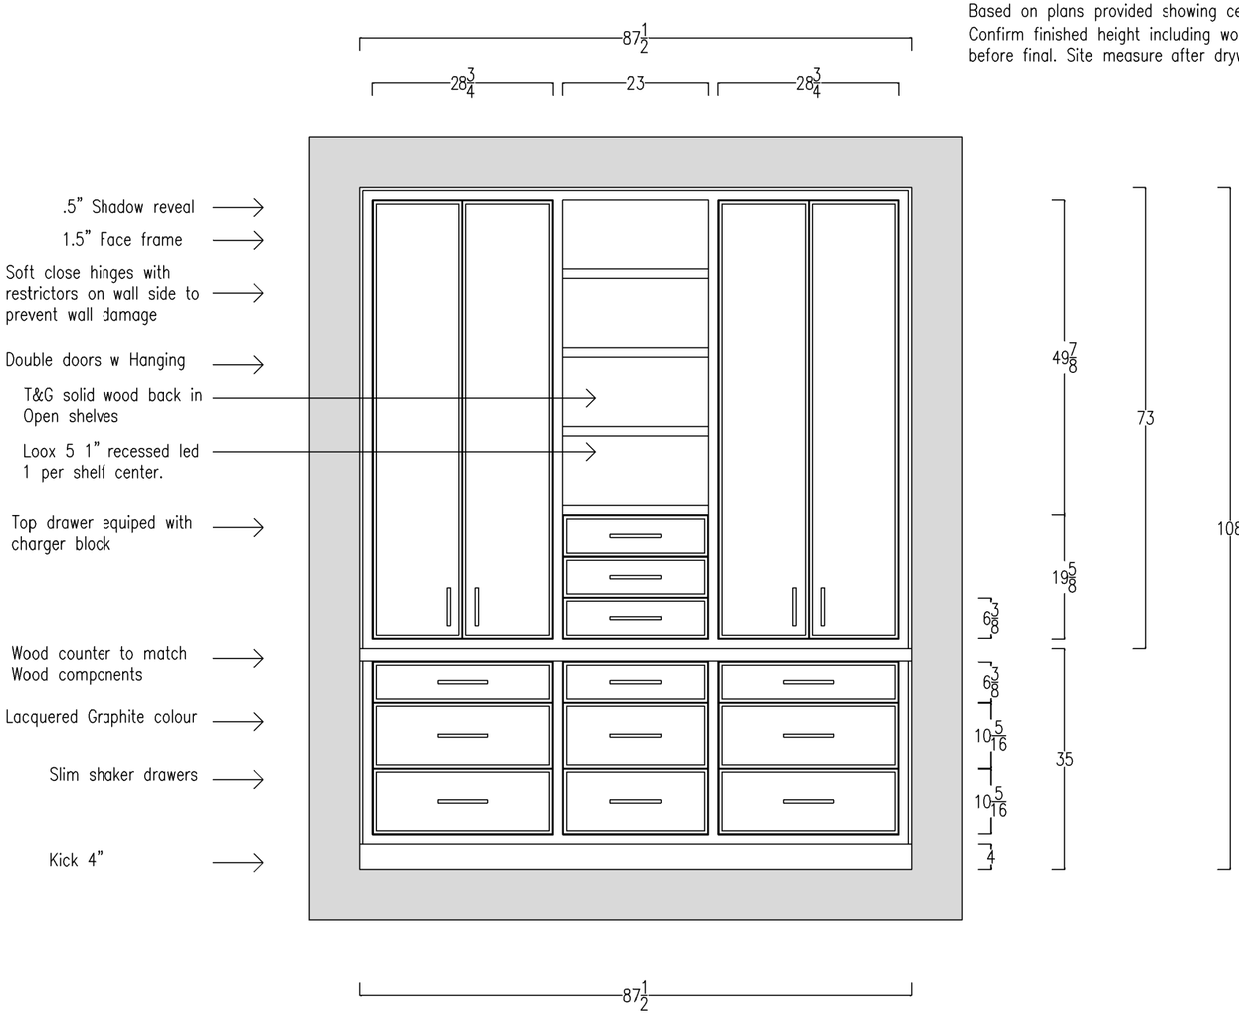

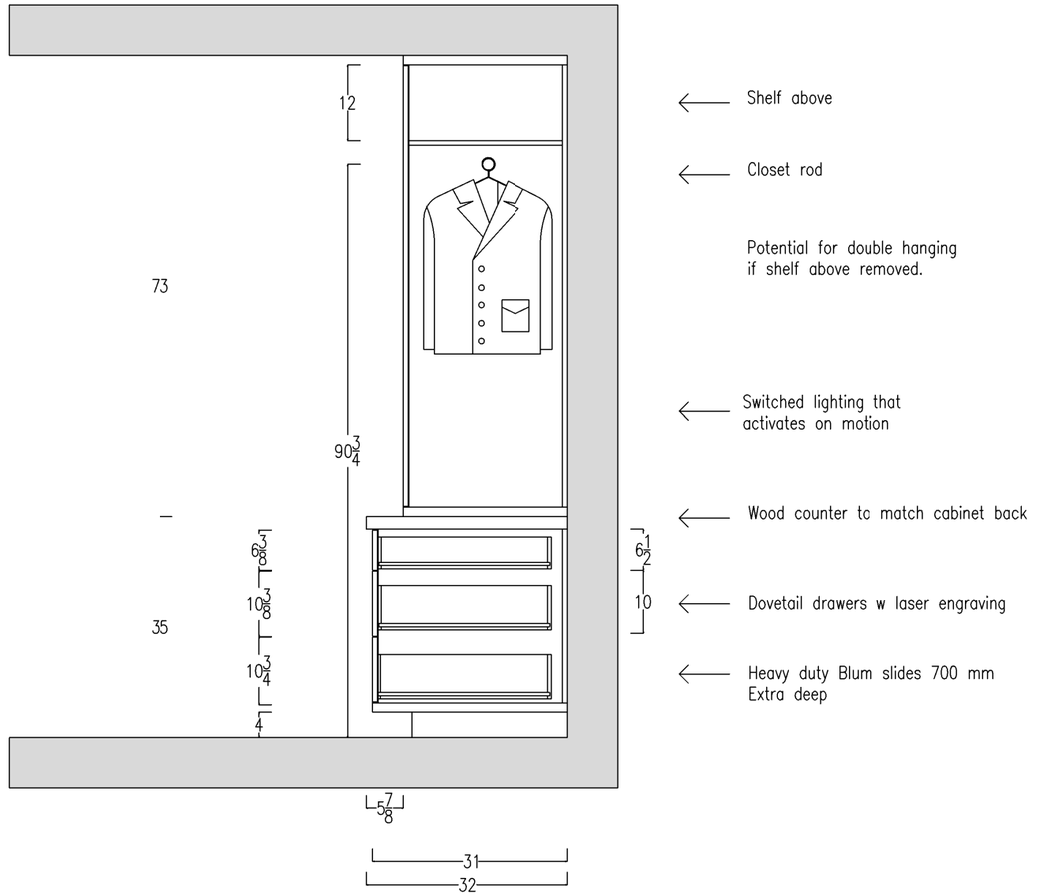

Fabi Residence -Bedroom Elevation


Scale: 1/2" : 1'

Sept 8,2026

Elevation A - 207.1

by William

Based on plans provided showing ceiling at 9 ft.
Confirm finished height including wood/carpet floor
before final. Site measure after drywall and flooring required.

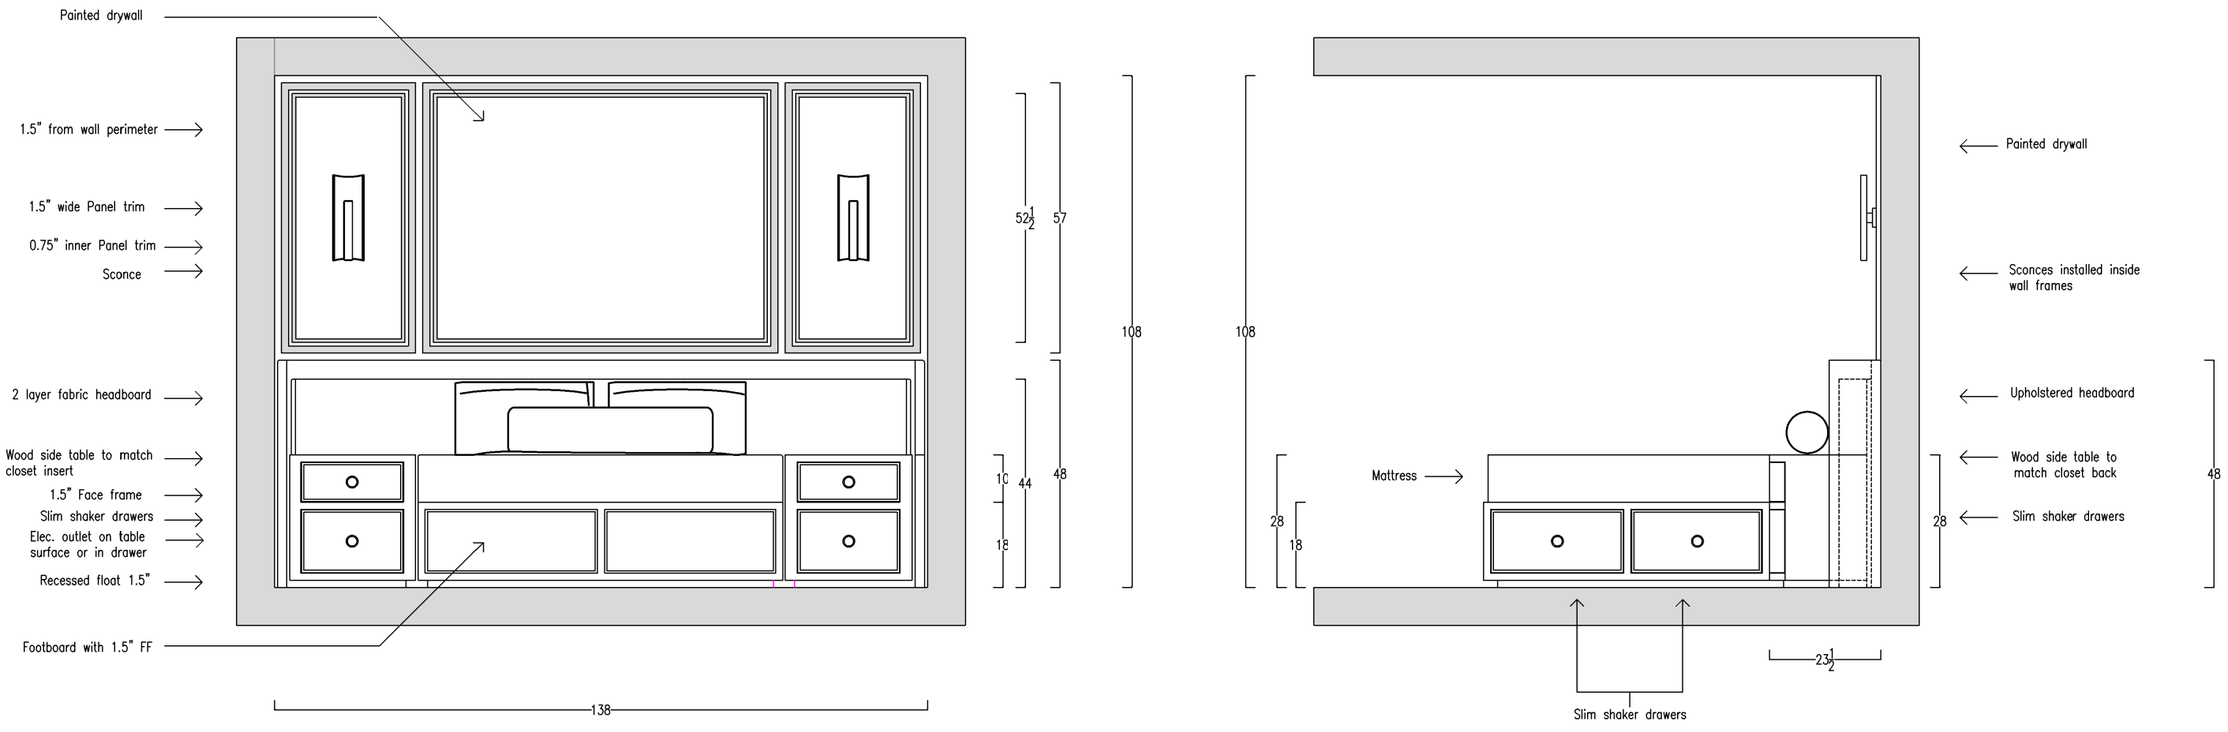

Fabi Residence -Bedroom Elevation


Scale: 3/8" : 1'

Sept 8,2026

Elevation B 207.2

by William

Based on plans provided showing ceiling at 9 ft.
Confirm finished height including wood/carpet floor
before final. Site measure after drywall and flooring required.

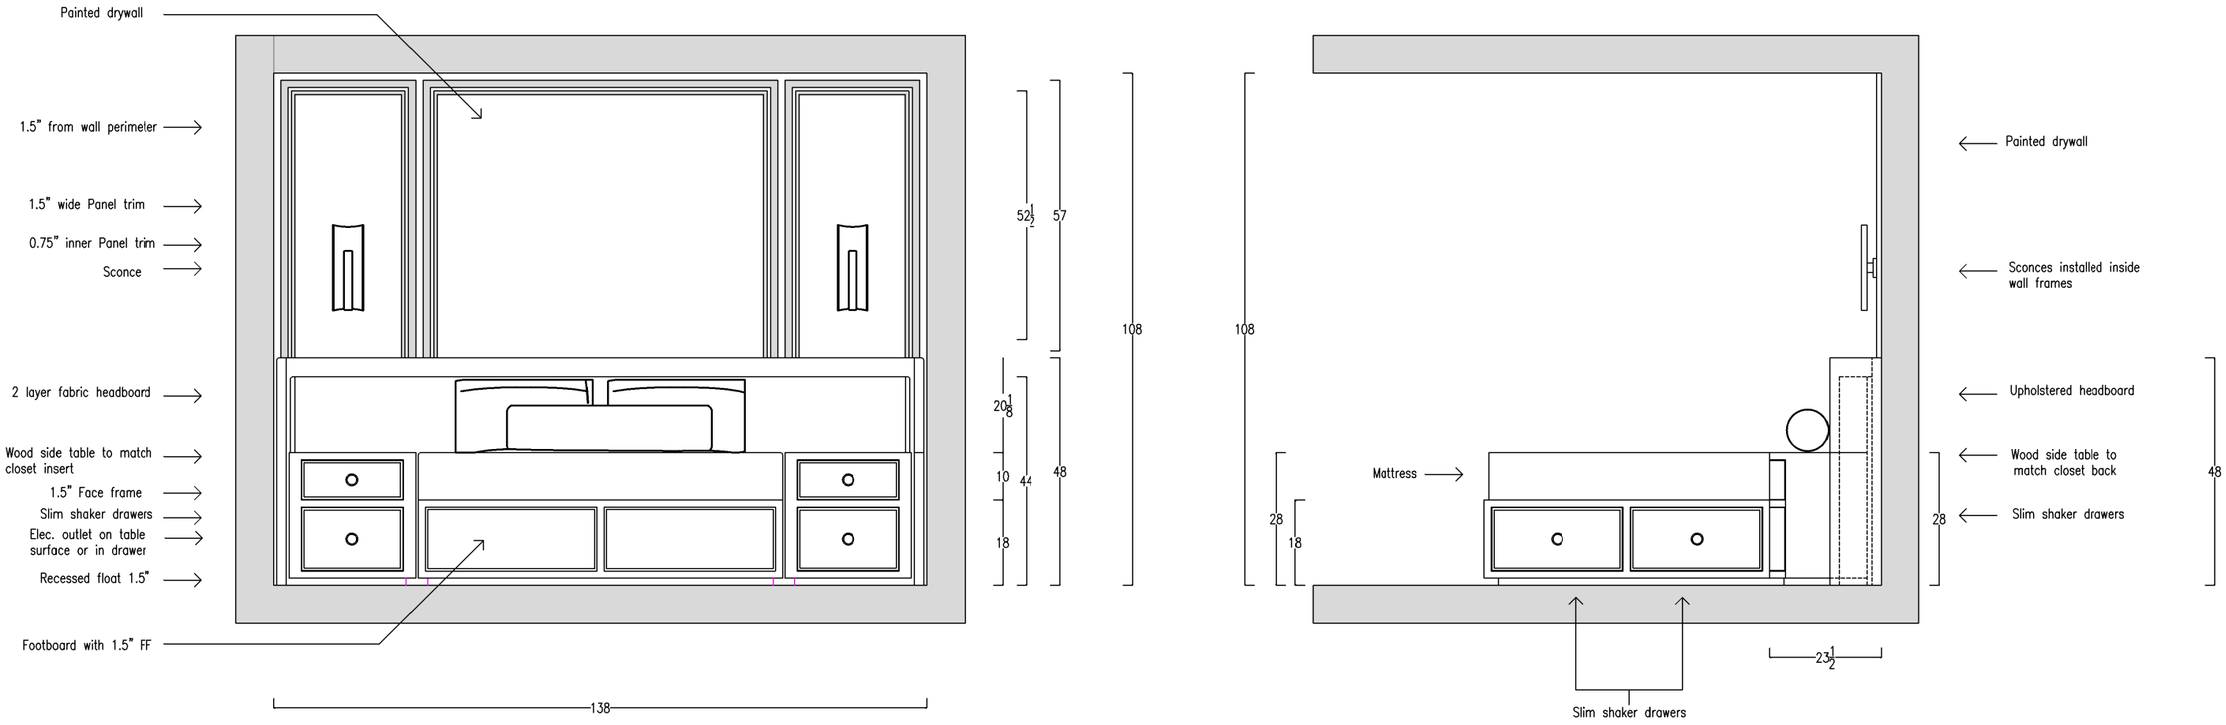

Fabi Residence -Bedroom Elevation


Scale: 3/8" : 1'


Sept 8,2026

Elevation B 207.2.1

by William

Based on plans provided showing ceiling at 9 ft.
Confirm finished height including wood/carpet floor
before final. Site measure after drywall and flooring required.

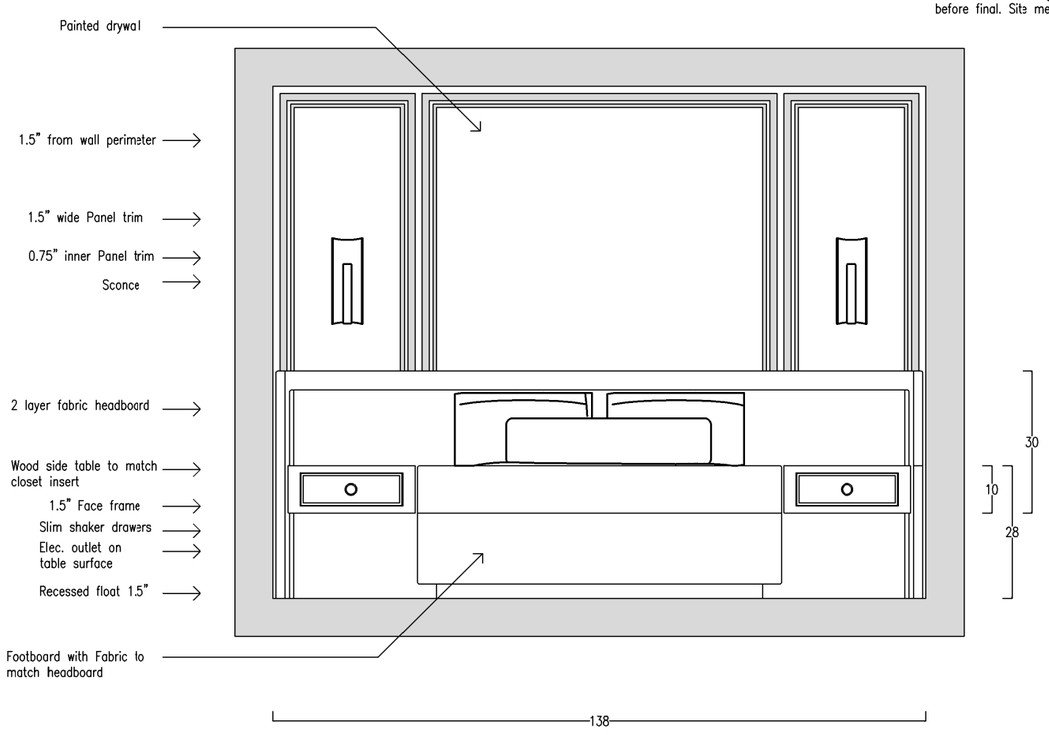

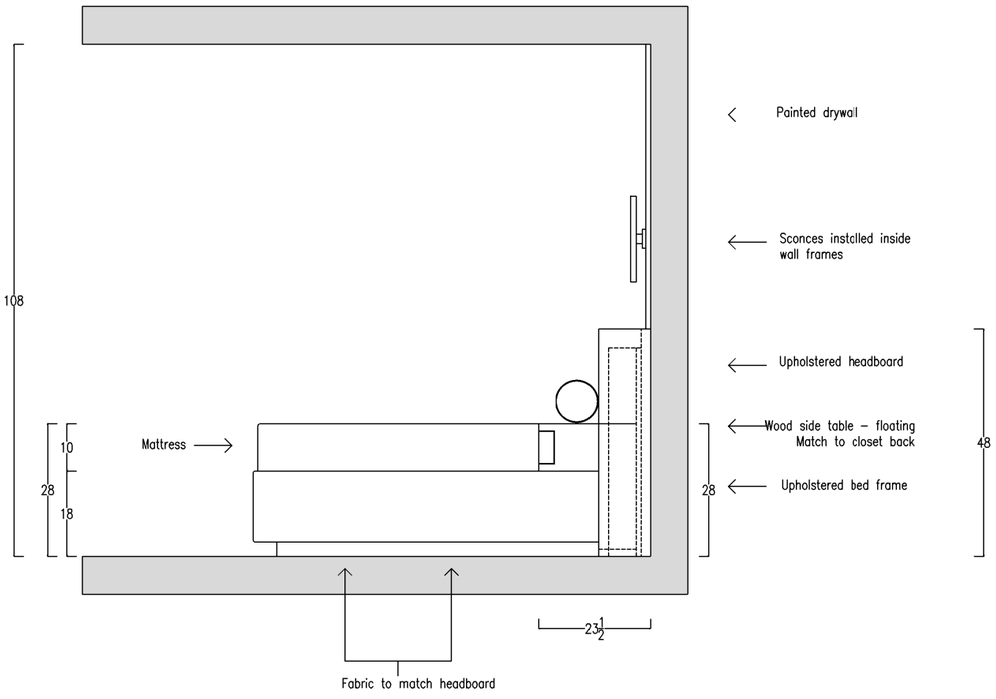


Fabi Residence -Bedroom Elevation

Scale: 3/8" : 1'

Sept 8,2026

Elevation B 207.2.2

by William

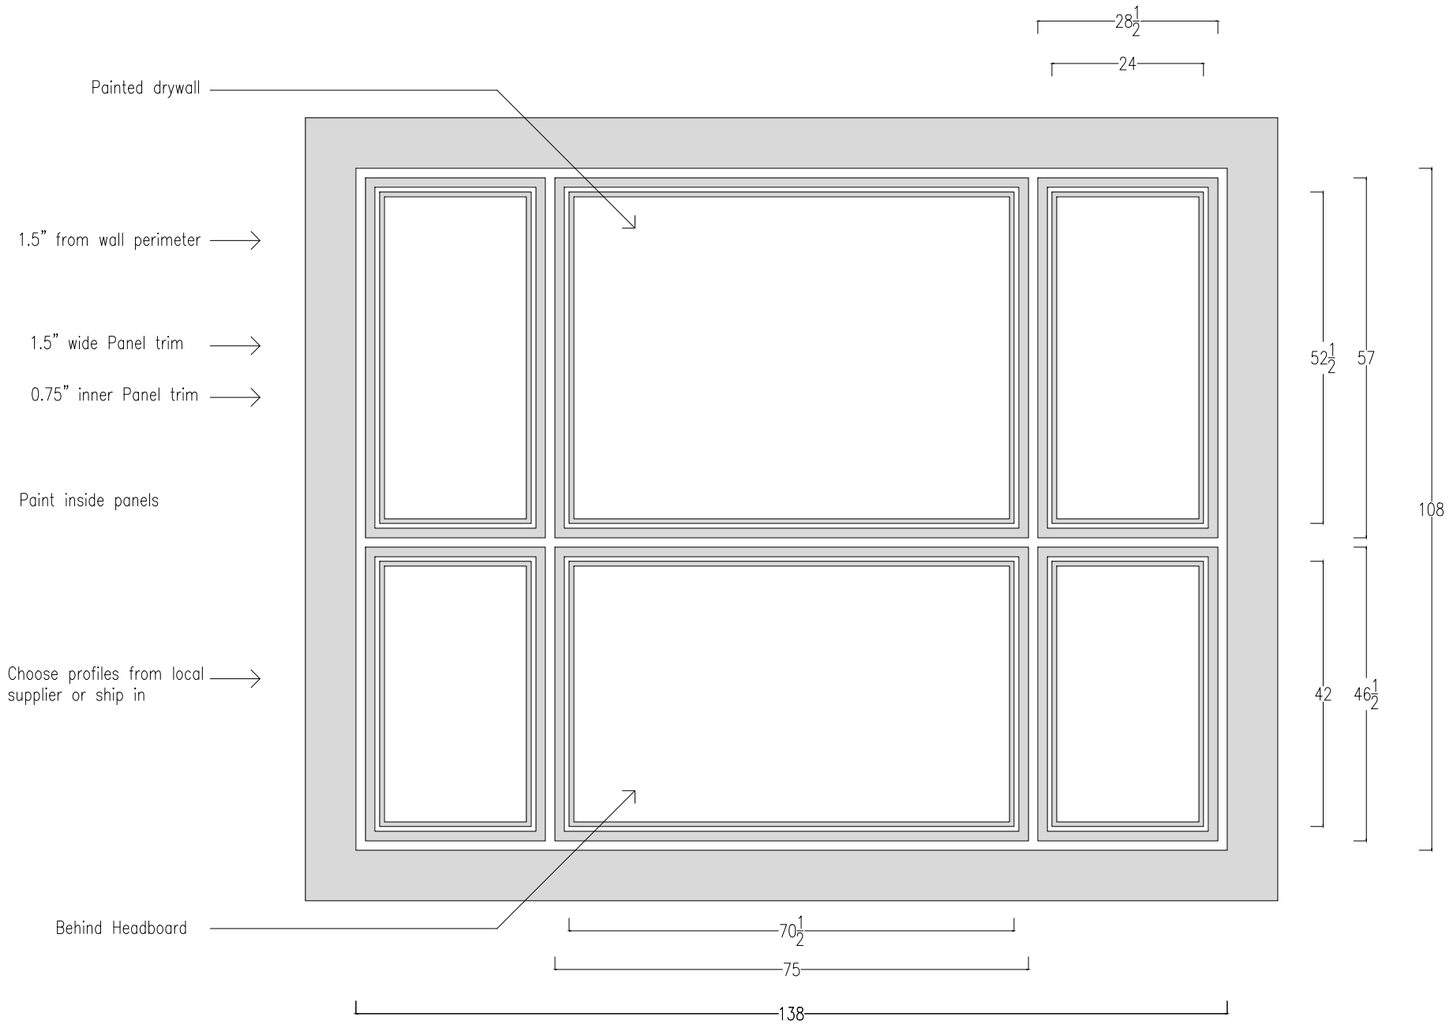


Fabi Residence -Bedroom Elevation

Scale: 1/2" : 1'

Sept 8,2026

Elevation C 207.3

by William

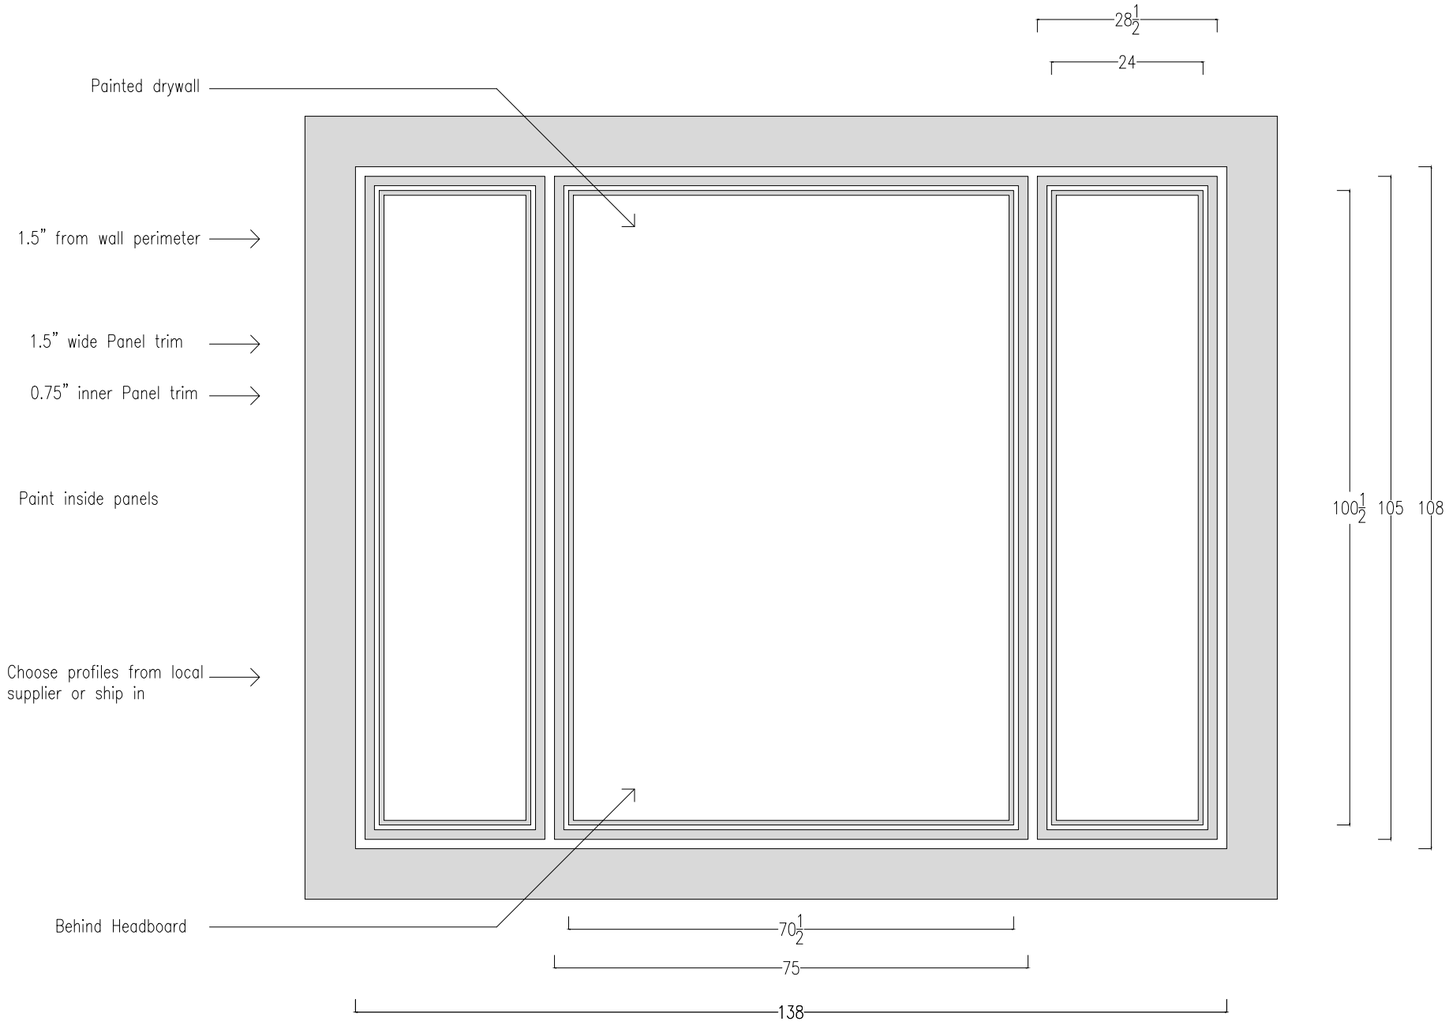

Fabi Residence -Bedroom Elevation


Scale: 1/2" : 1'

Sept 8,2026

Elevation C 207.3.1

by William

Round sidetablesand curved headboard made either
in solid wood using staves
Or with wiggle board core under veneer or ccn cut ribs,

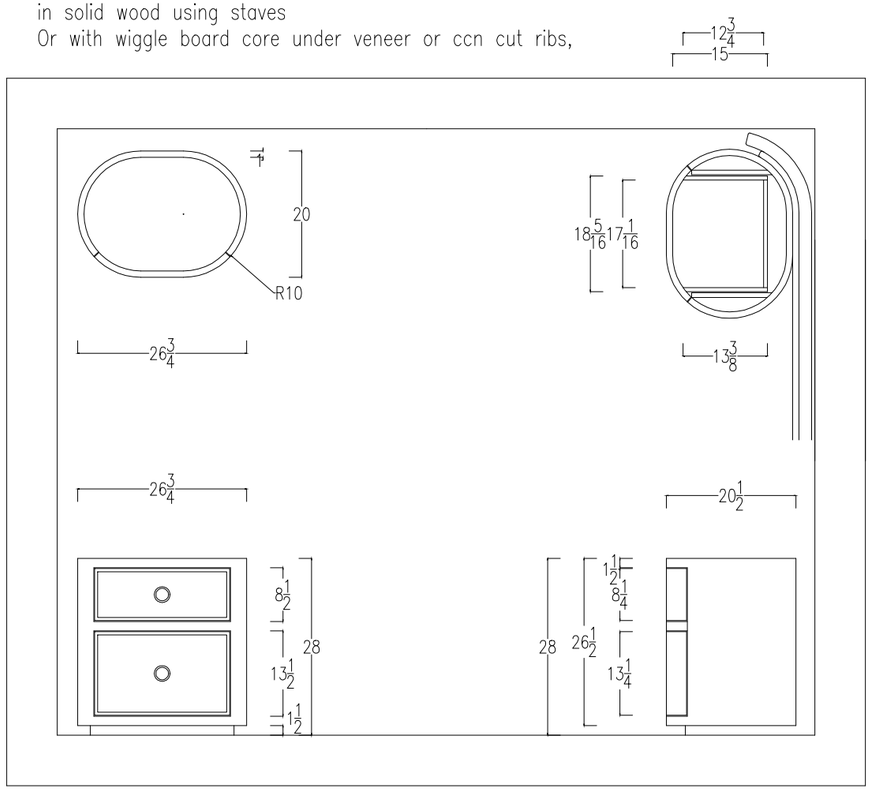

Drawer with 200mm Blum slides.
Mortise and tenon into drawer face

Drawer equiped with charging dock
or Elec. outlet on table top.
Optional wall mount outlet nearby.

Drawer faces to coordinate with
slim shaker faces throughout or
be slab to accentuate curve.
Turned pulls in Brushed brash
or custom turned wood.

Devise mechanism to anchor
to headboard.

Fabi Residence -Bedroom Elevation

Scale: 1/2" : 1'

Sept 8,2026

Detail D 207.4