by William

8'-4 3/4"

10'-6"

H - 42.75
S - 44

LED light strip with non visible profile rabetted into Bevel frame.

B 201.2

33 1/8 | 58 3/4 | 34 1/8

Brass edged shelves installed to stud through stone

Brushed brass faucet

Stone counter to match backsplash

Intergrated stone sink

2" bevelled border framing the assembly

Storage

ge acccess.

”

airs

16

9

24 1/8 26 28

2

19

23

26

30 | 12 | 16 1/2 | 30 | 30

Euro-Cargo II
Recycling Center
Product # 8461412100

B 201.2

A 201.1

Slim Shaker wood door with brass Pull.
Posible brass laminate panel

Bar Lounge

201


Fabi Residence - WetBar Plan


Scale: 3/4" : 1'

Sept 3,2026

Plan view - 201.0

by William

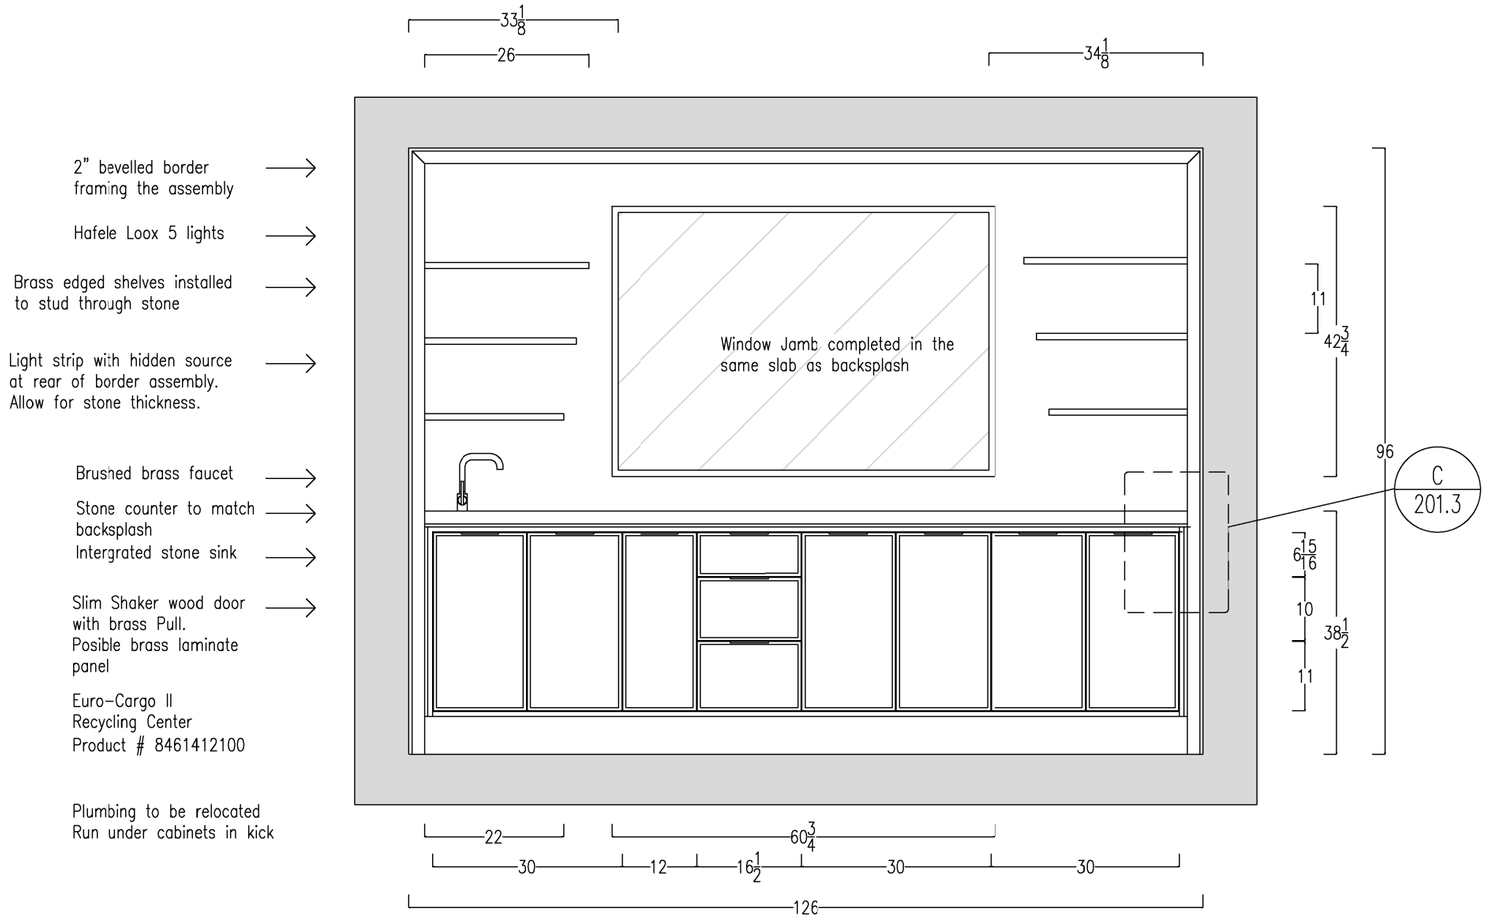

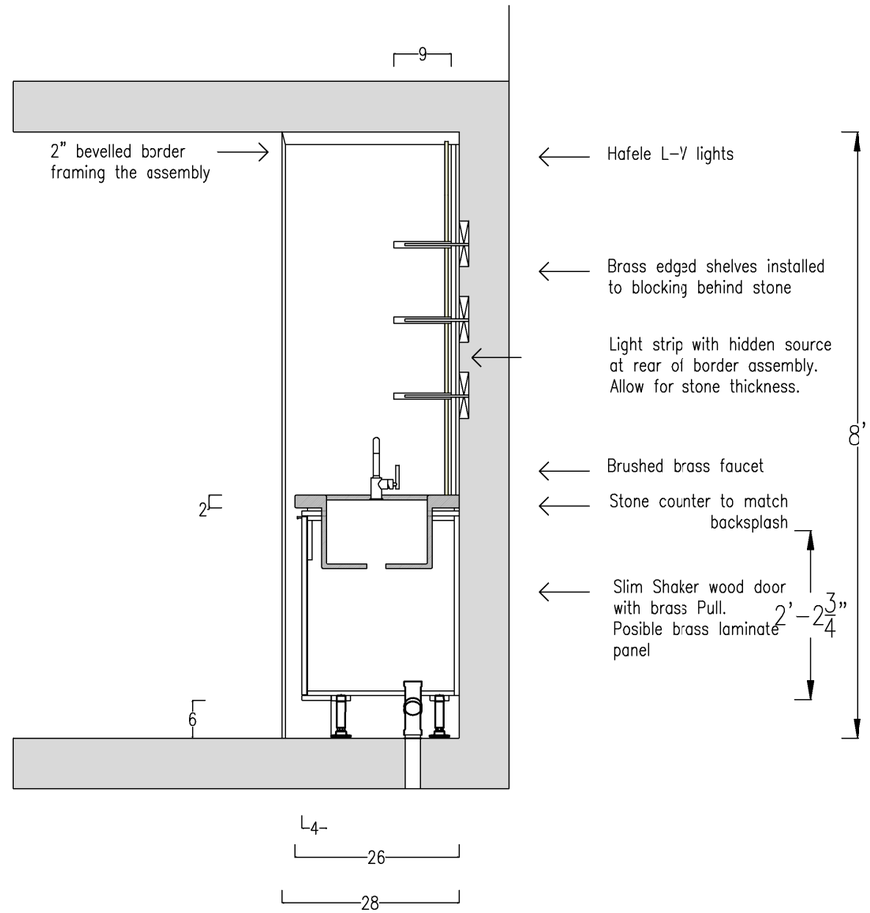


Fabi Residence - WetBar Plan


Scale: 1/2" : 1'

Sept 3,2026

Elevation A - 201.1

by William

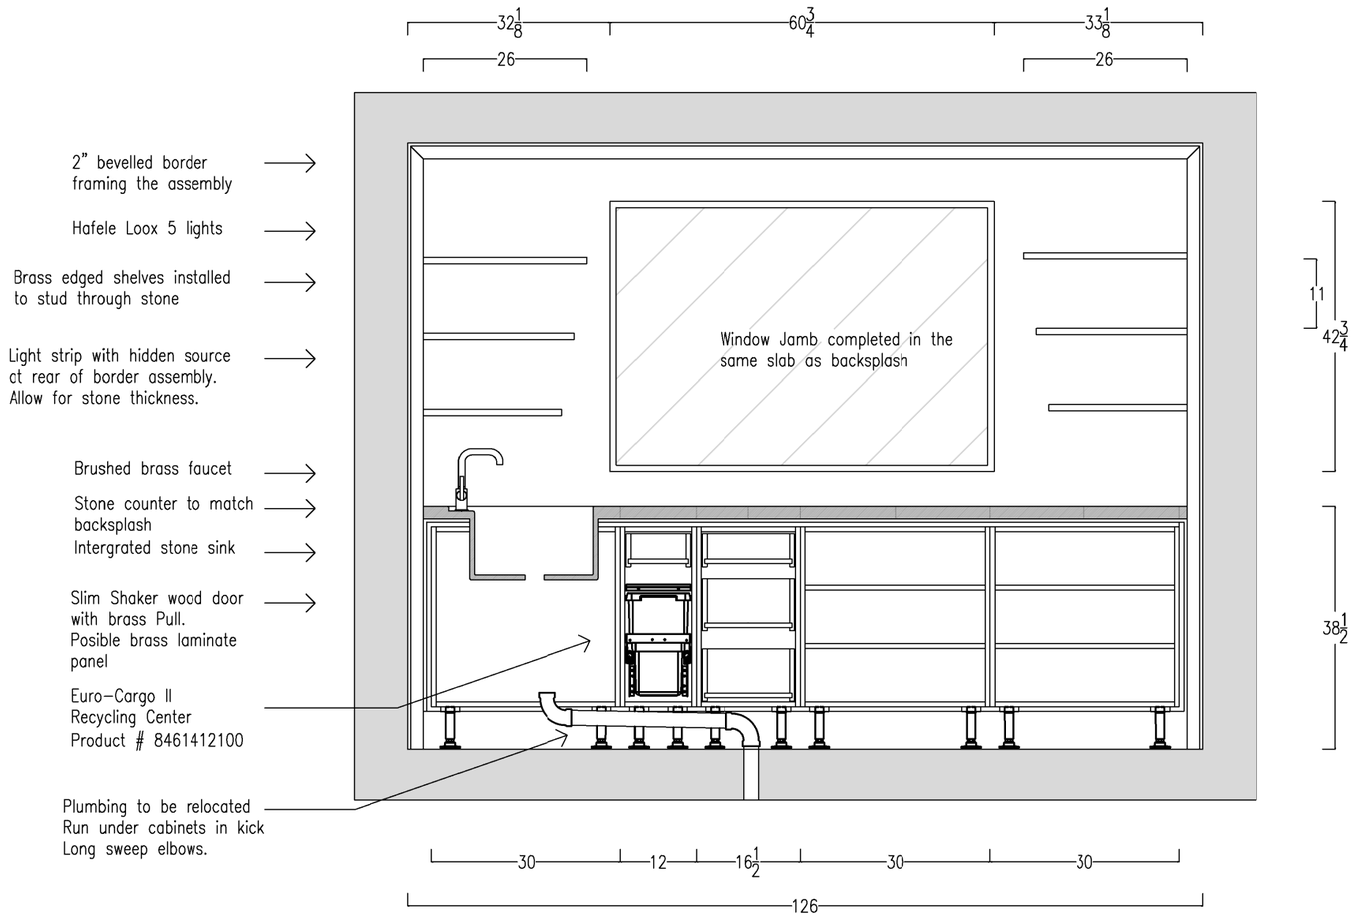

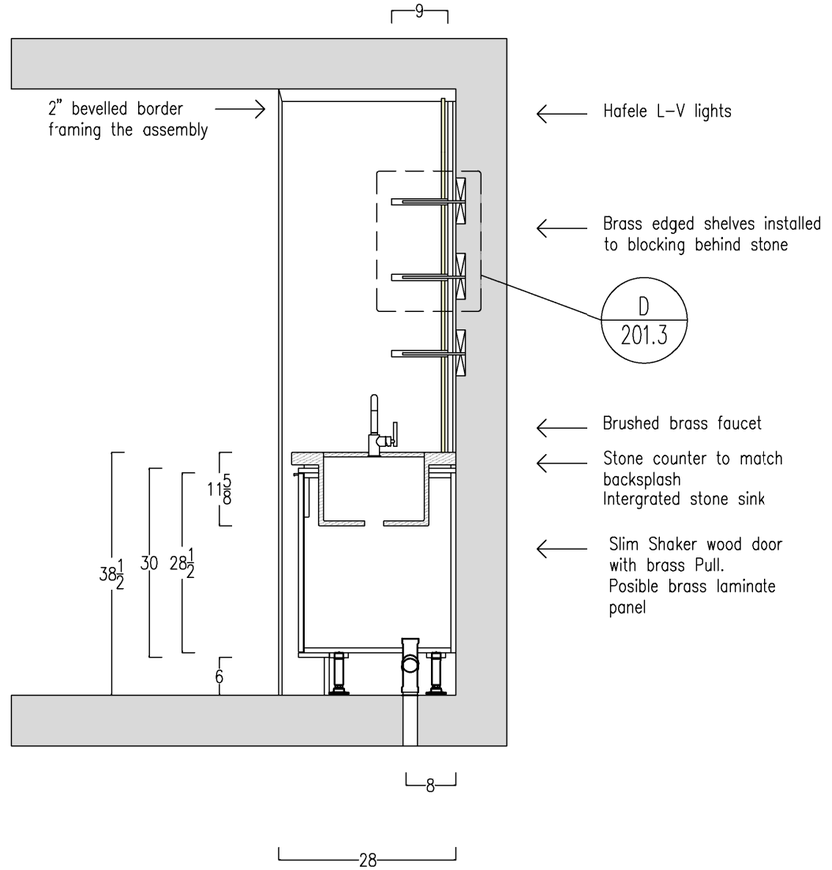

Fabi Residence - WetBar Plan


Scale: 1/2" : 1'


Sept 3,2026


Elevation B 201.2

by William

D Wall Shelf
1” = 1’

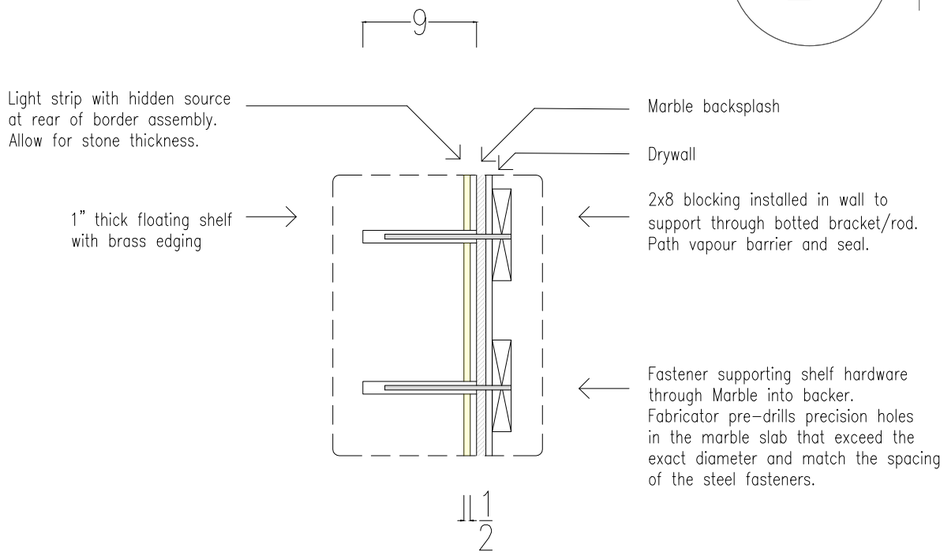

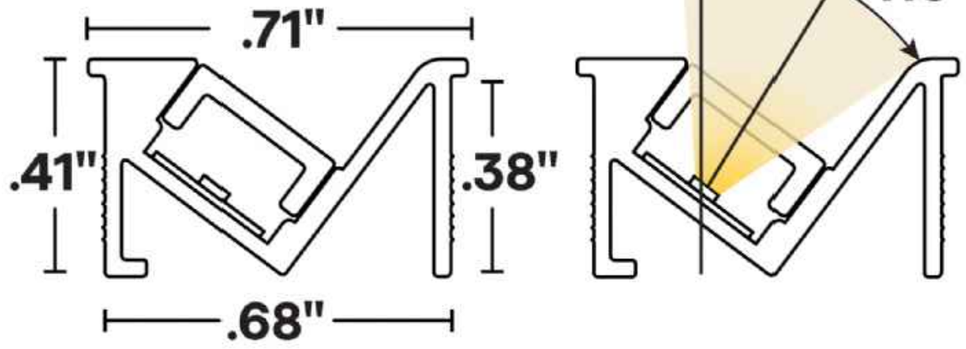

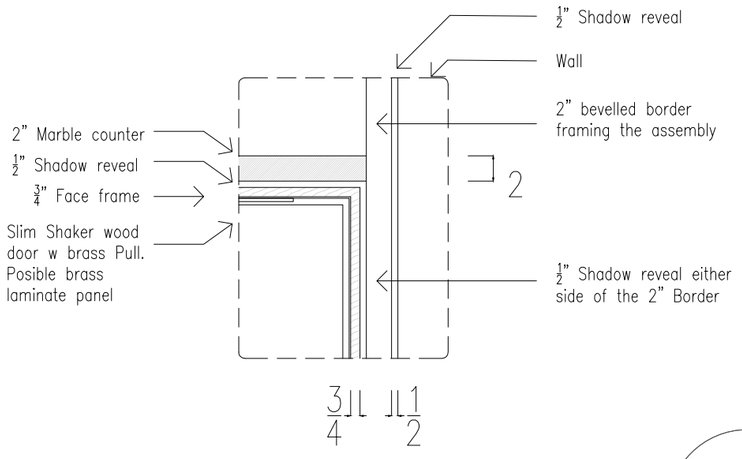

C Face detail
1” = 1’

C Light Detail
MICRO 5 KICKER–FLAT

Fabi Residence - WetBar Plan

Scale: 1/2" : 1'

Sept 3,2026

Detail C D E 201.3

by William



Fabi Residence - WetBar Plan

Sept 3,2026

Render 201.4